

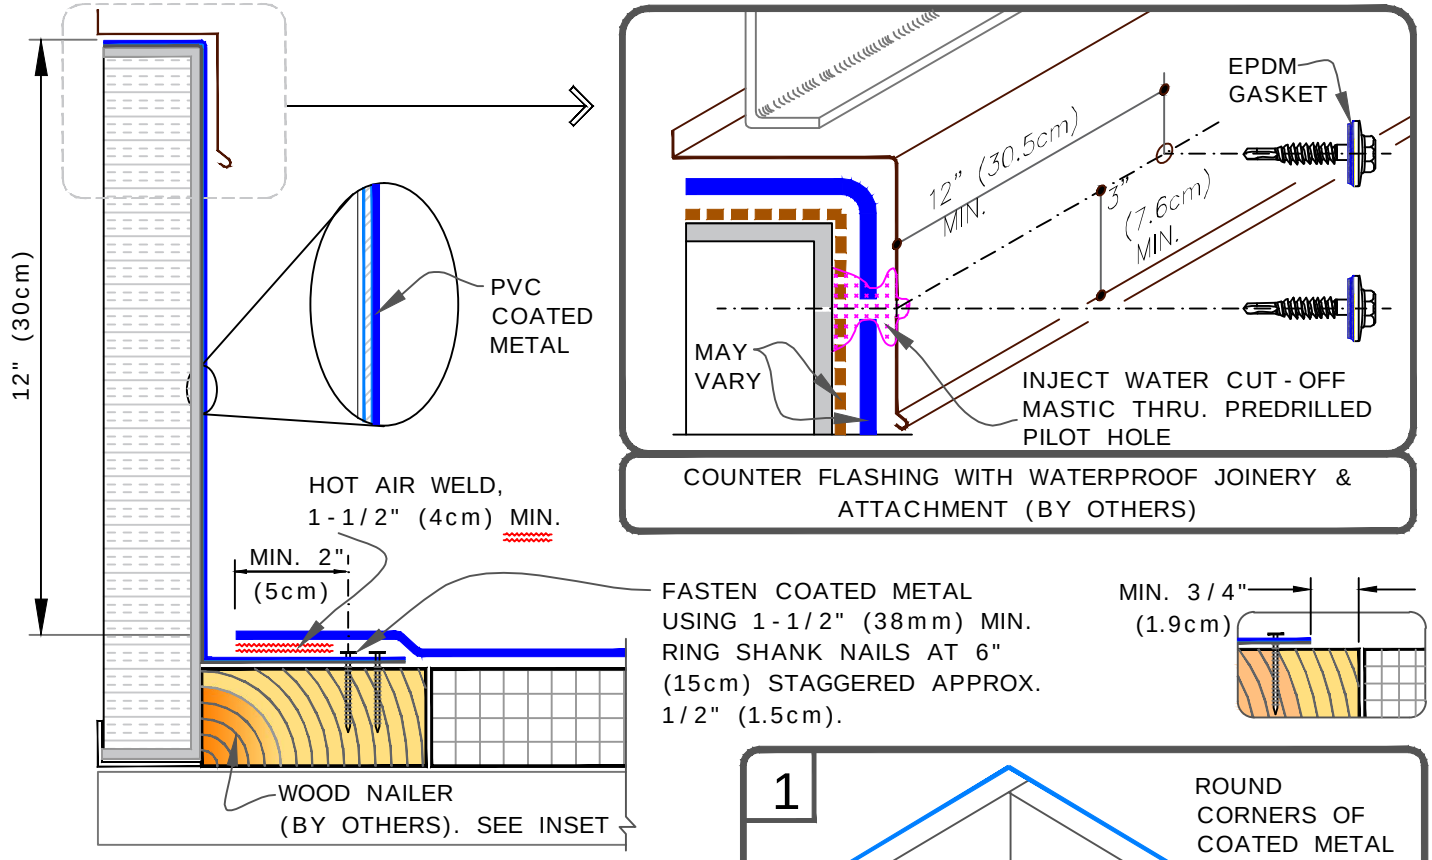


SEQUENCE:

1. 3" (7.6cm) REINFORCED MEMBRANE STRIPPING.
2. FIELD MEMBRANE.
3. TOP 6" (15.2cm) NON-REINFORCED MEMBRANE STRIPPING.

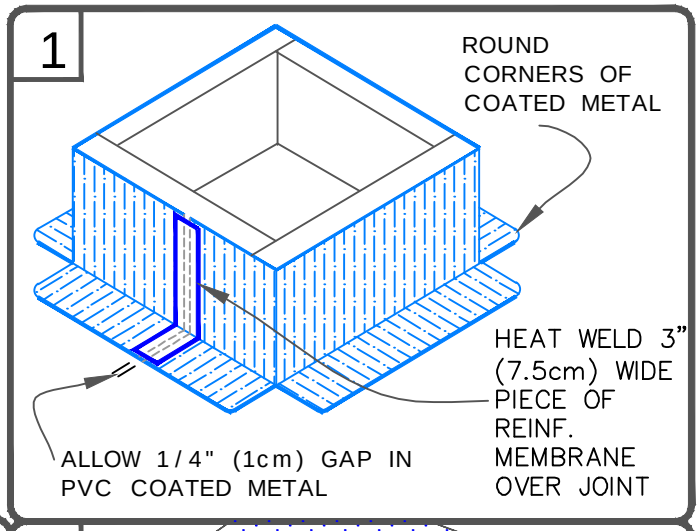

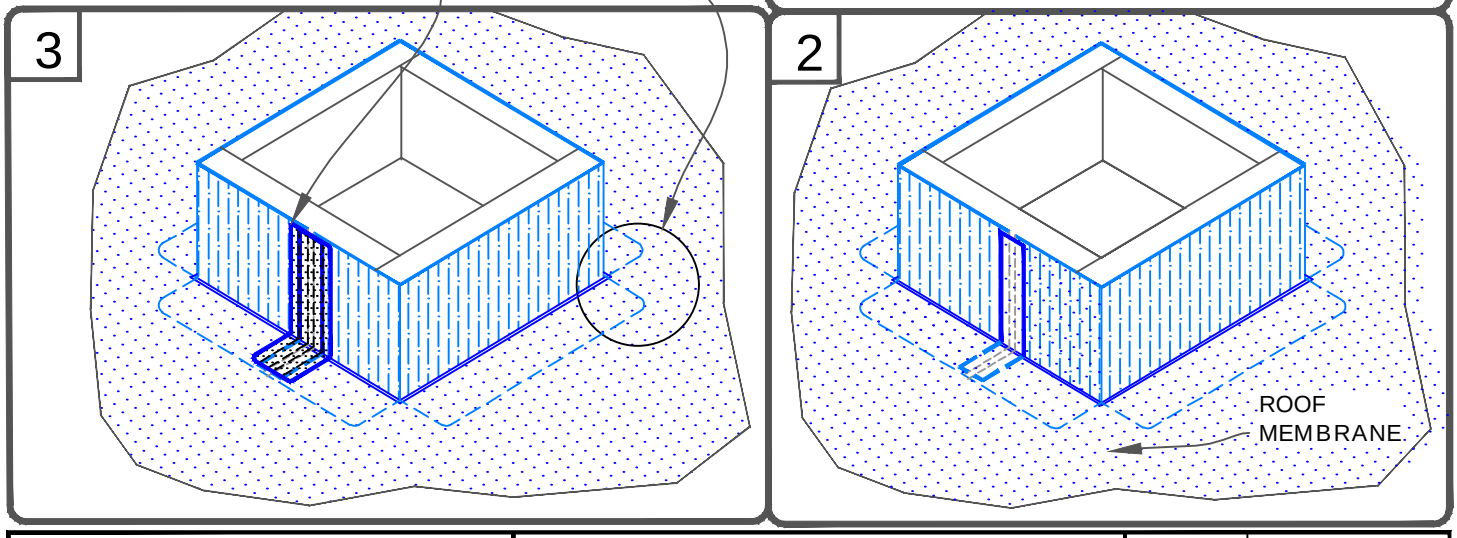

CARLISLE SYNTEC SYSTEMS

CURB FLASHING WITH PVC COATED METAL

MAXIMUM WARRANTY: 30 YEARS

PVC

DETAIL NO.

U - 5B

U (Universal Detail)

© 2026 CARLISLE SynTec a division of CARLISLE Construction Materials Incorporated